

|              |  |
|--------------|--|
| Инв. № подл. |  |
| Подп. и дата |  |
| Взам. инв. № |  |

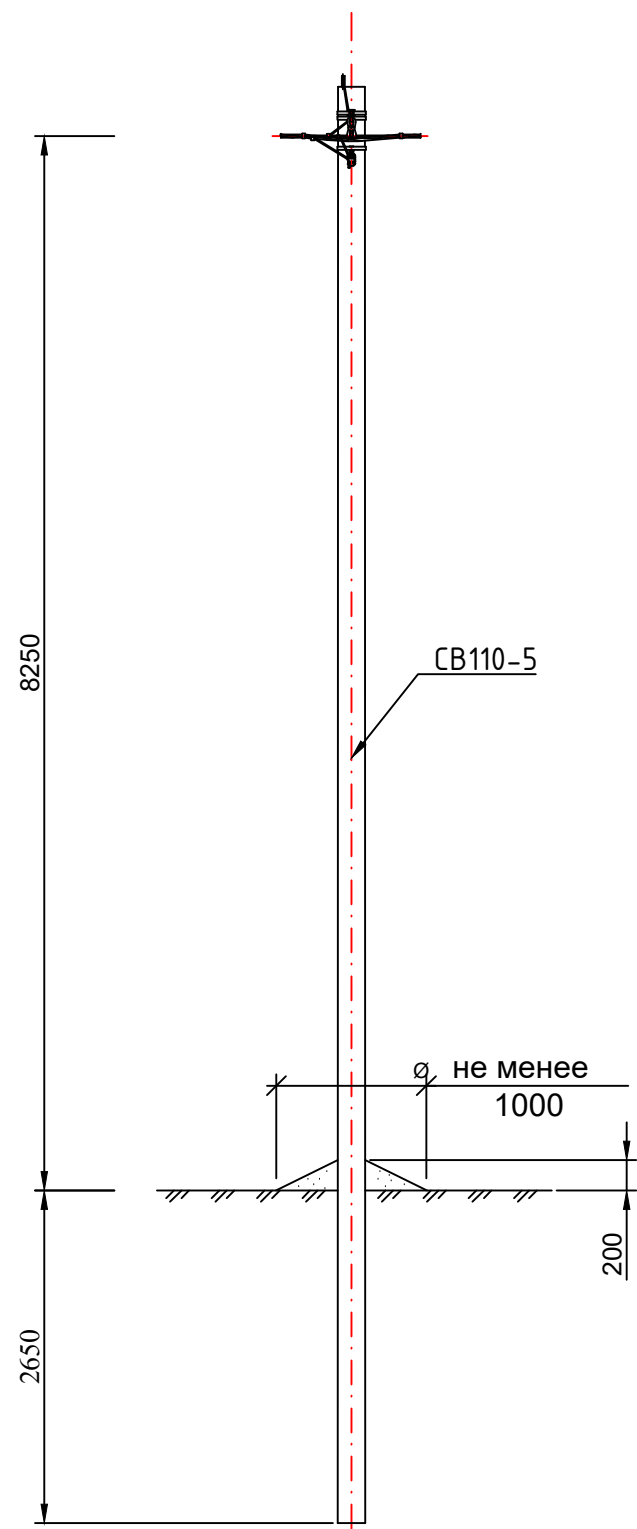


Схема установки стойки  
CB110-5 (промежуточная опора)

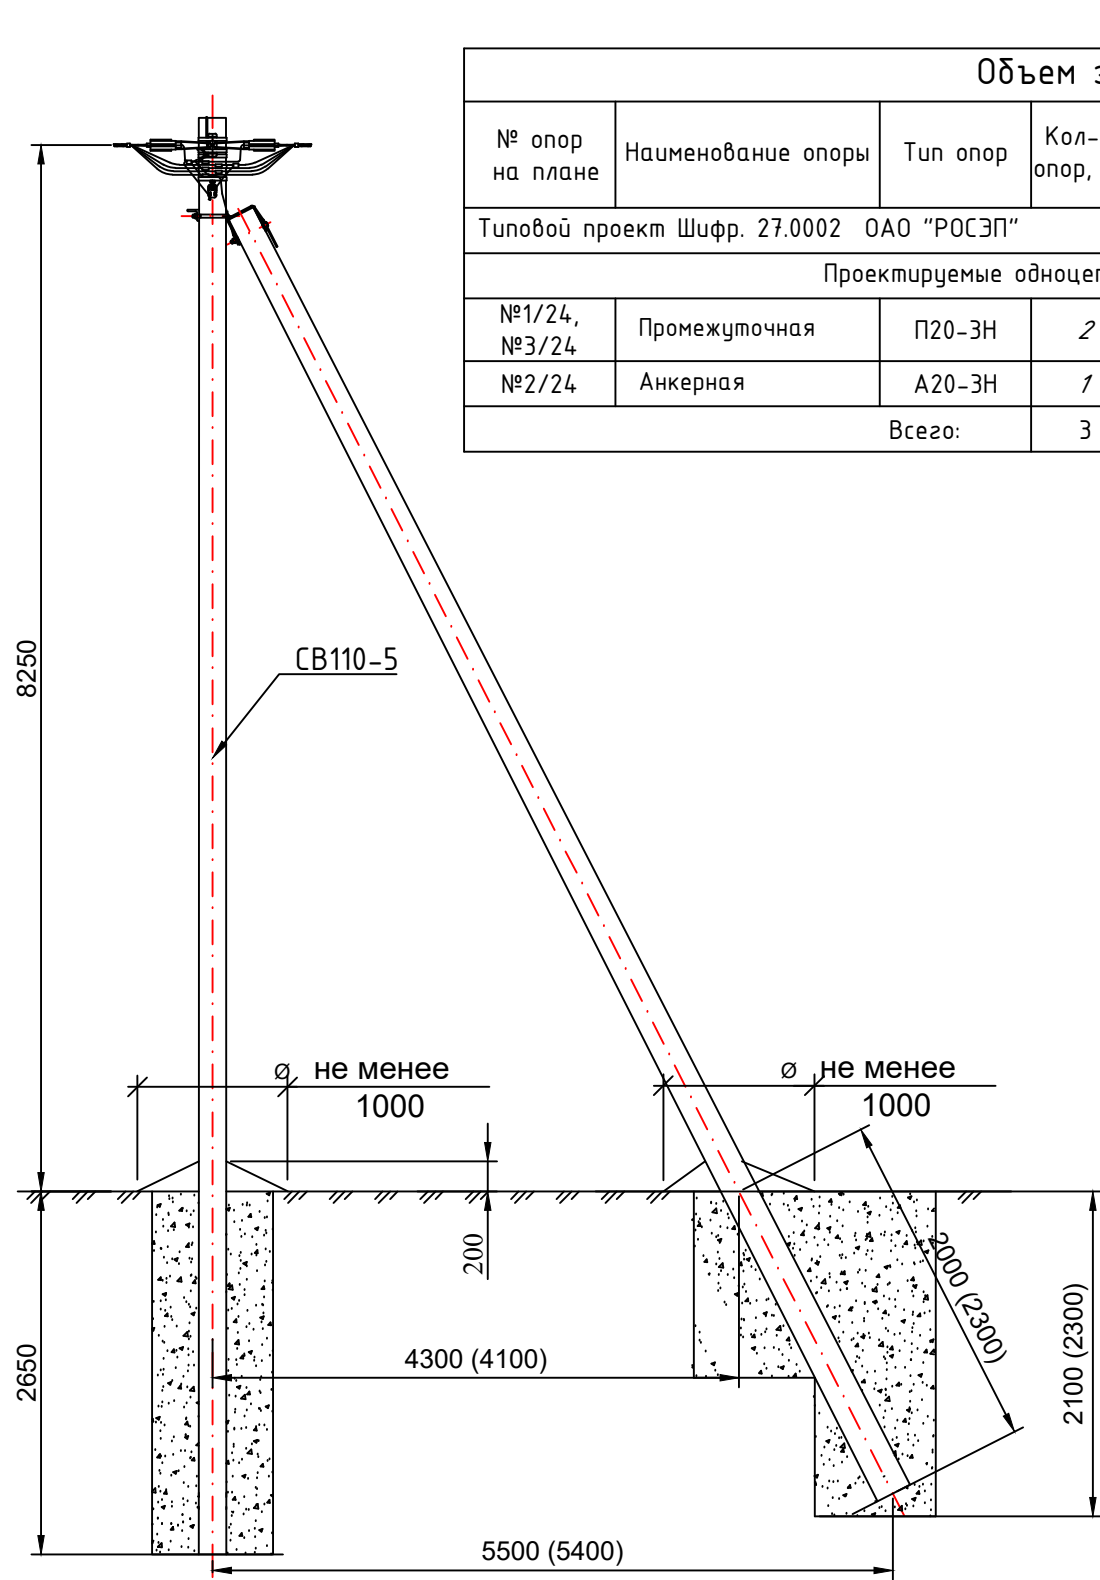


Схема установки стойки  
CB110-5 (анкерная опора)

| Объем засыпки под осадку земли              |                    |          |                 |                        |                                                               |                       |
|---------------------------------------------|--------------------|----------|-----------------|------------------------|---------------------------------------------------------------|-----------------------|
| № опор на плане                             | Наименование опоры | Тип опор | Кол-во опор, шт | Кол-во стоек всего, шт | объем земли на стойку, м³ (V=π·R²·h, V=3,14·0,5²·0,2=0,628м³) | Общий объем земли, м³ |
| Типовой проект Шифр. 27.0002 ОАО "РОСЭП"    |                    |          |                 |                        |                                                               |                       |
| Проектируемые одноцепные опоры ВЛИ-0,4 кВкВ |                    |          |                 |                        |                                                               |                       |
| №1/24, №3/24                                | Промежуточная      | П20-3Н   | 2               | 2                      | 0.628                                                         | 1.256                 |
| №2/24                                       | Анкерная           | А20-3Н   | 1               | 2                      | 0.628                                                         | 1.256                 |
| Всего:                                      |                    |          | 3               | 4                      |                                                               | 2.512                 |

|              |         |      |        |         |      |   |  |  |                                                                                         |      |        |
|--------------|---------|------|--------|---------|------|---|--|--|-----------------------------------------------------------------------------------------|------|--------|
|              |         |      |        |         |      | 4 708-308092-125-11/24.   |  |  |                                                                                         |      |        |
|              |         |      |        |         |      | Строительство ТП – 6/0,4кВ, ВЛЗ-6 кВ от ВЛЗ-6кВ ф. ЦРП-48 – ТП-326 ПС №387 “Подрезково”, ВЛИ-0,38 кВ, рлр, ВРЩ-0,4 кВ, в т.ч. ПИР, МО, Химкинский р-н, г. Химки |  |  |                                                                                         |      |        |
| Изм.         | Кол.уч. | Лист | № док. | Подпись | Дата |   |  |  |                                                                                         |      |        |
|              |         |      |        |         |      | Внешнее электроснабжение   |  |  | Стадия                                                                                  | Лист | Листов |
| Стр.контроль | Русин   |      |        |         |      |   |  |  | ИД                                                                                      | 1    | 1      |
| Прораб       | Волков  |      |        |         |      | Исполнительная схема устройства опор   |  |  | Общество с ограниченной ответственностью<br>"ЭНЕРГОСИСТЕМЫ"<br>телефон 8(926) 334-34-34 |      |        |
|              |         |      |        |         |      |   |  |  |                                                                                         |      |        |