


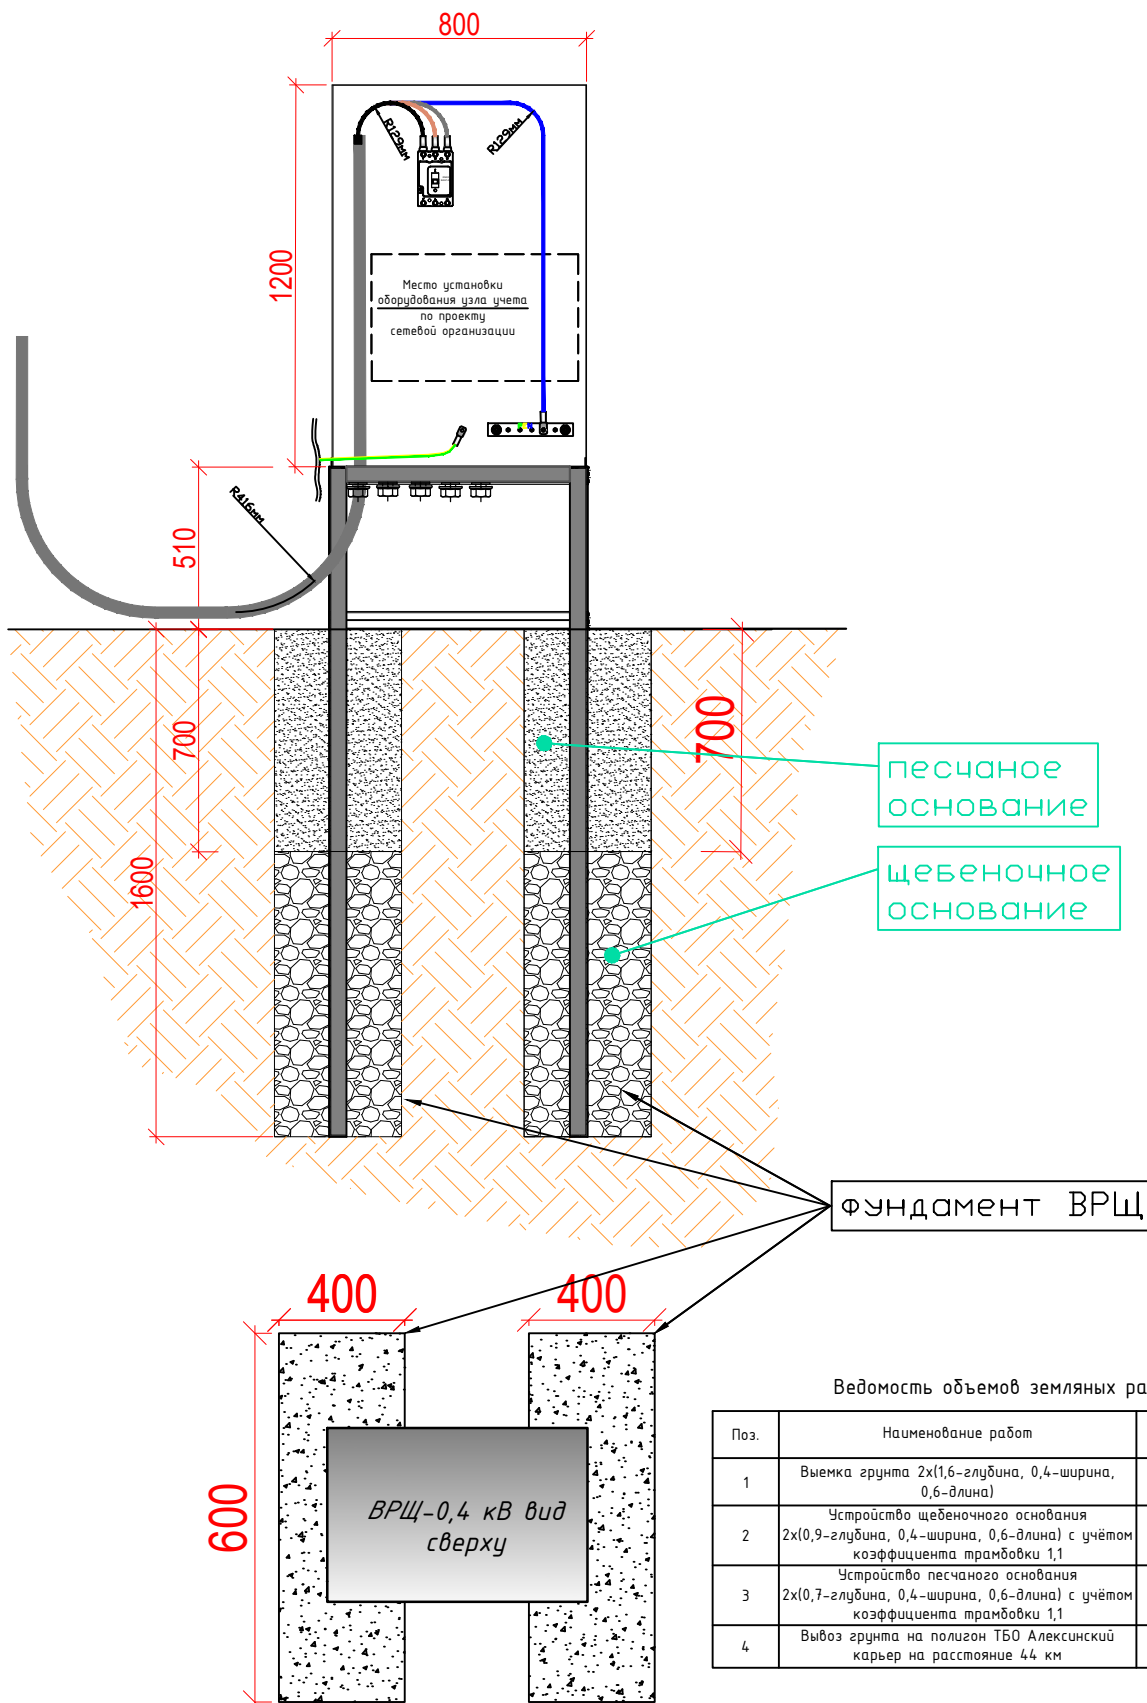

Ведомость объемов земляных работ

| Поз. | Наименование работ                                                                                          | Ед. изер. | Кол.        |
|------|---|-----------|-------------|
| 1    | Выемка грунта 2х(1,6-глубина, 0,4-ширина, 0,6-длина)                                                        | м³        | 0.768       |
| 2    | Устройство щебеночного основания 2х(0,9-глубина, 0,4-ширина, 0,6-длина) с учётом коэффициента трамбовки 1,1 | м³        | 0.475       |
| 3    | Устройство песчаного основания 2х(0,7-глубина, 0,4-ширина, 0,6-длина) с учётом коэффициента трамбовки 1,1   | м³        | 0.370       |
| 4    | Вывоз грунта на полигон ТБО Алексинский карьер на расстояние 44 км                                          | м³/т      | 0,768/0,998 |

|   |         |      |        |                                                                                   |      |
|---|---------|------|--------|-----------------------------------------------------------------------------------|------|
| Взам. инв. №   |         |      |        |                                                                                   |      |
| Подп. и дата   |         |      |        |                                                                                   |      |
| Инв. № подл.   |         |      |        |                                                                                   |      |
| Изм.   | Кол.уч. | Лист | № док. | Подпись                                                                           | Дата |
| Стр.контроль   | Русин   |      |        |                                                                                   |      |
| Прораб   | Волков  |      |        |                                                                                   |      |
| 4 708-308092-125-11/24.   |         |      |        |                                                                                   |      |
| Строительство ТП - 6/0,4кВ, ВЛЗ-6 кВ от ВЛЗ-6кВ ф. ЦРП-48 - ТП-326 ПС №387 "Подрезково", ВЛИ-0,38 кВ, рлр, ВРЩ-0,4 кВ, в т.ч. ПИР, МО, Химкинский р-н, г. Химки |         |      |        |                                                                                   |      |
| Внешнее электроснабжение   |         |      |        | Стадия                                                                            | Лист |
|   |         |      |        | ИД                                                                                | 1    |
| Исполнительная схема постамента ВРЩ-0,4 кВ   |         |      |        | Общество с ограниченной ответственностью "ЭНЕРГОСИСТЕМЫ" телефон 8(926) 334-34-34 |      |