
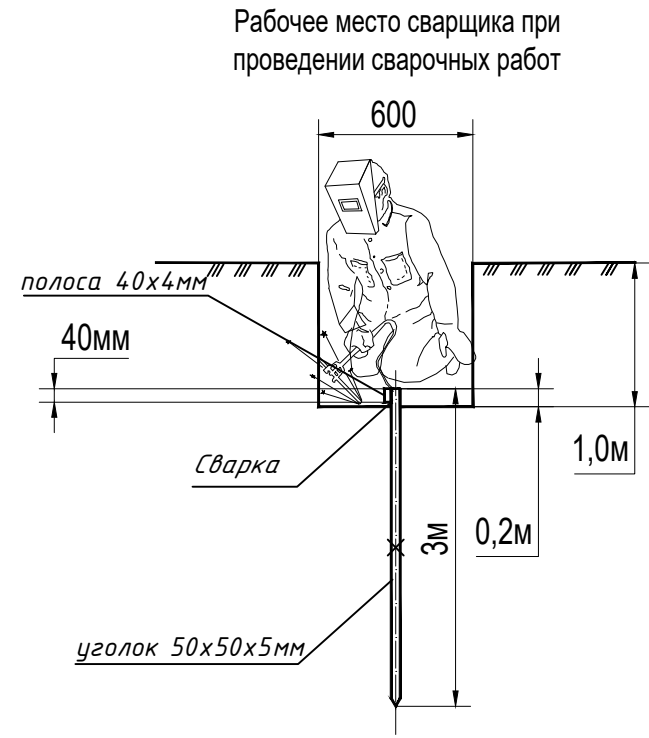
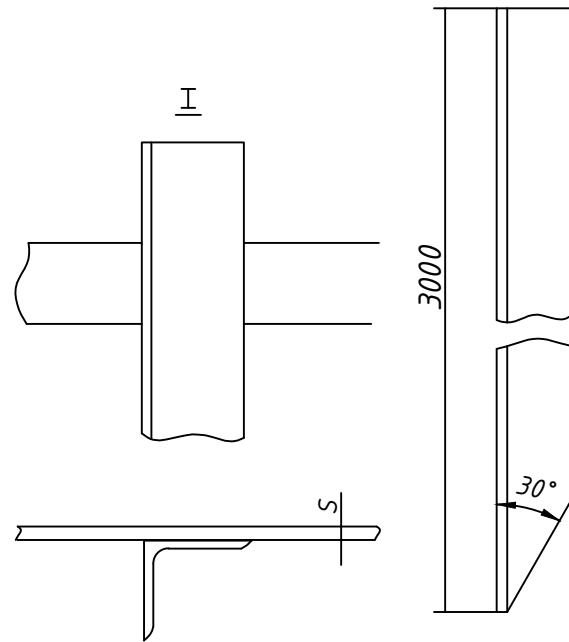


Инв. № подл.	Подп. и дата	Взам. инв. №

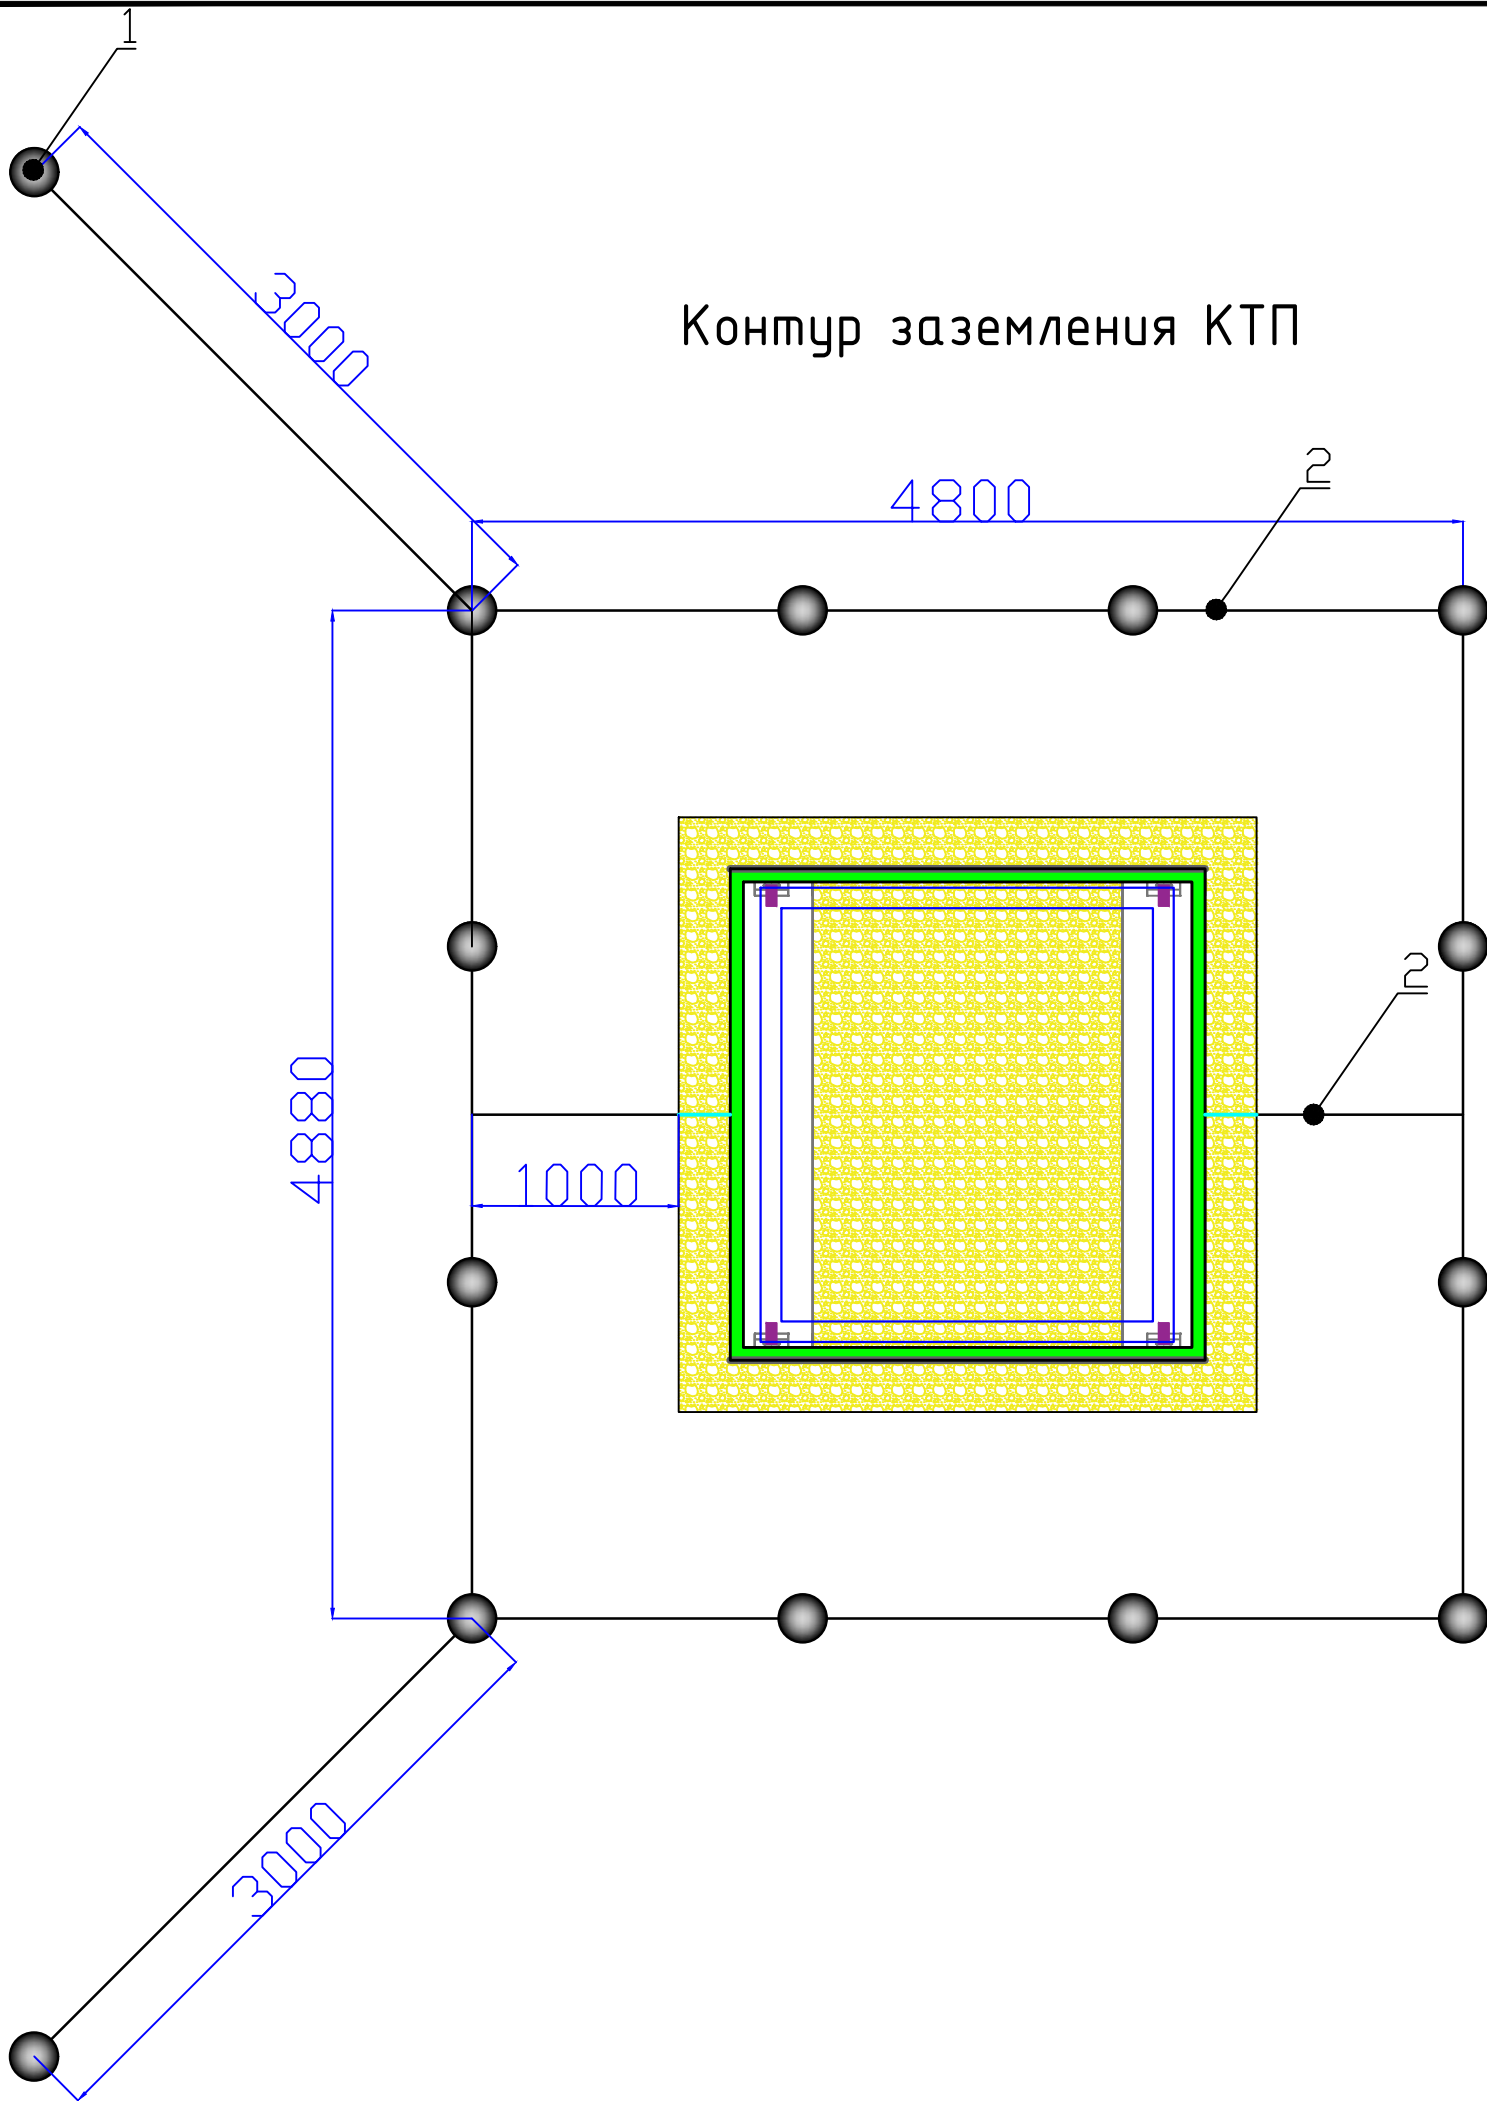

Ведомость узлов установки электрического оборудования

Поз.	Обознач. или тип изделия	Наименование	Длина, м	Вес ед.,кг	Вес всего,кг	Примеч.
1	ГОСТ 8509-93	Уголок 50х50х5 (L=3,0м), м	42	3,77	158.34	14 шт.
2	ГОСТ 103-2006	Полоса стальная 40х4, м	27.36	1,256	34.36	в траншее
Итого:					192.70	

Ведомость объемов земляных работ

Поз.	Наименование работ	Ед. изм.	Кол-во, на 1 опору, м3
1	Выемка грунта 1,0м-глубина, 0,6м-ширина основания траншеи (минимальная ширина траншеи для выполнения сварочных работ по привариванию горизонтального заземлителя к вертикальному электроду), (2х4,88+2х4,8+2х3+2х1)=27.36м-длина)	м³	16.42
2	Обратная засыпка грунта	м³	16.42

						4 708-308092-125-11/24.				
						Строительство ТП - 6/0,4кВ, В/З-6 кВ от В/З-6кВ ф. ЦРП-48 - ТП-326 ПС №387 "Подрезково", В/Л-0,38 кВ, р/л, ВРЩ-0,4 кВ, в т.ч. ПИР, МО, Химкинский р-н, г. Химки				
Изм.	Кол.уч.	Лист	№ док.	Подпись	Дата					
Стр.контроль	Русин					Внешнее электроснабжение		Стadia	Лист	Листов
Прораб	Волков					Исполнительная схема заземления КТП-1542		ИД	1	1
						Исполнительная схема заземления КТП-1542		Общество с ограниченной ответственностью "ЭНЕРГОСИСТЕМЫ" телефон 8(926) 334-34-34		