


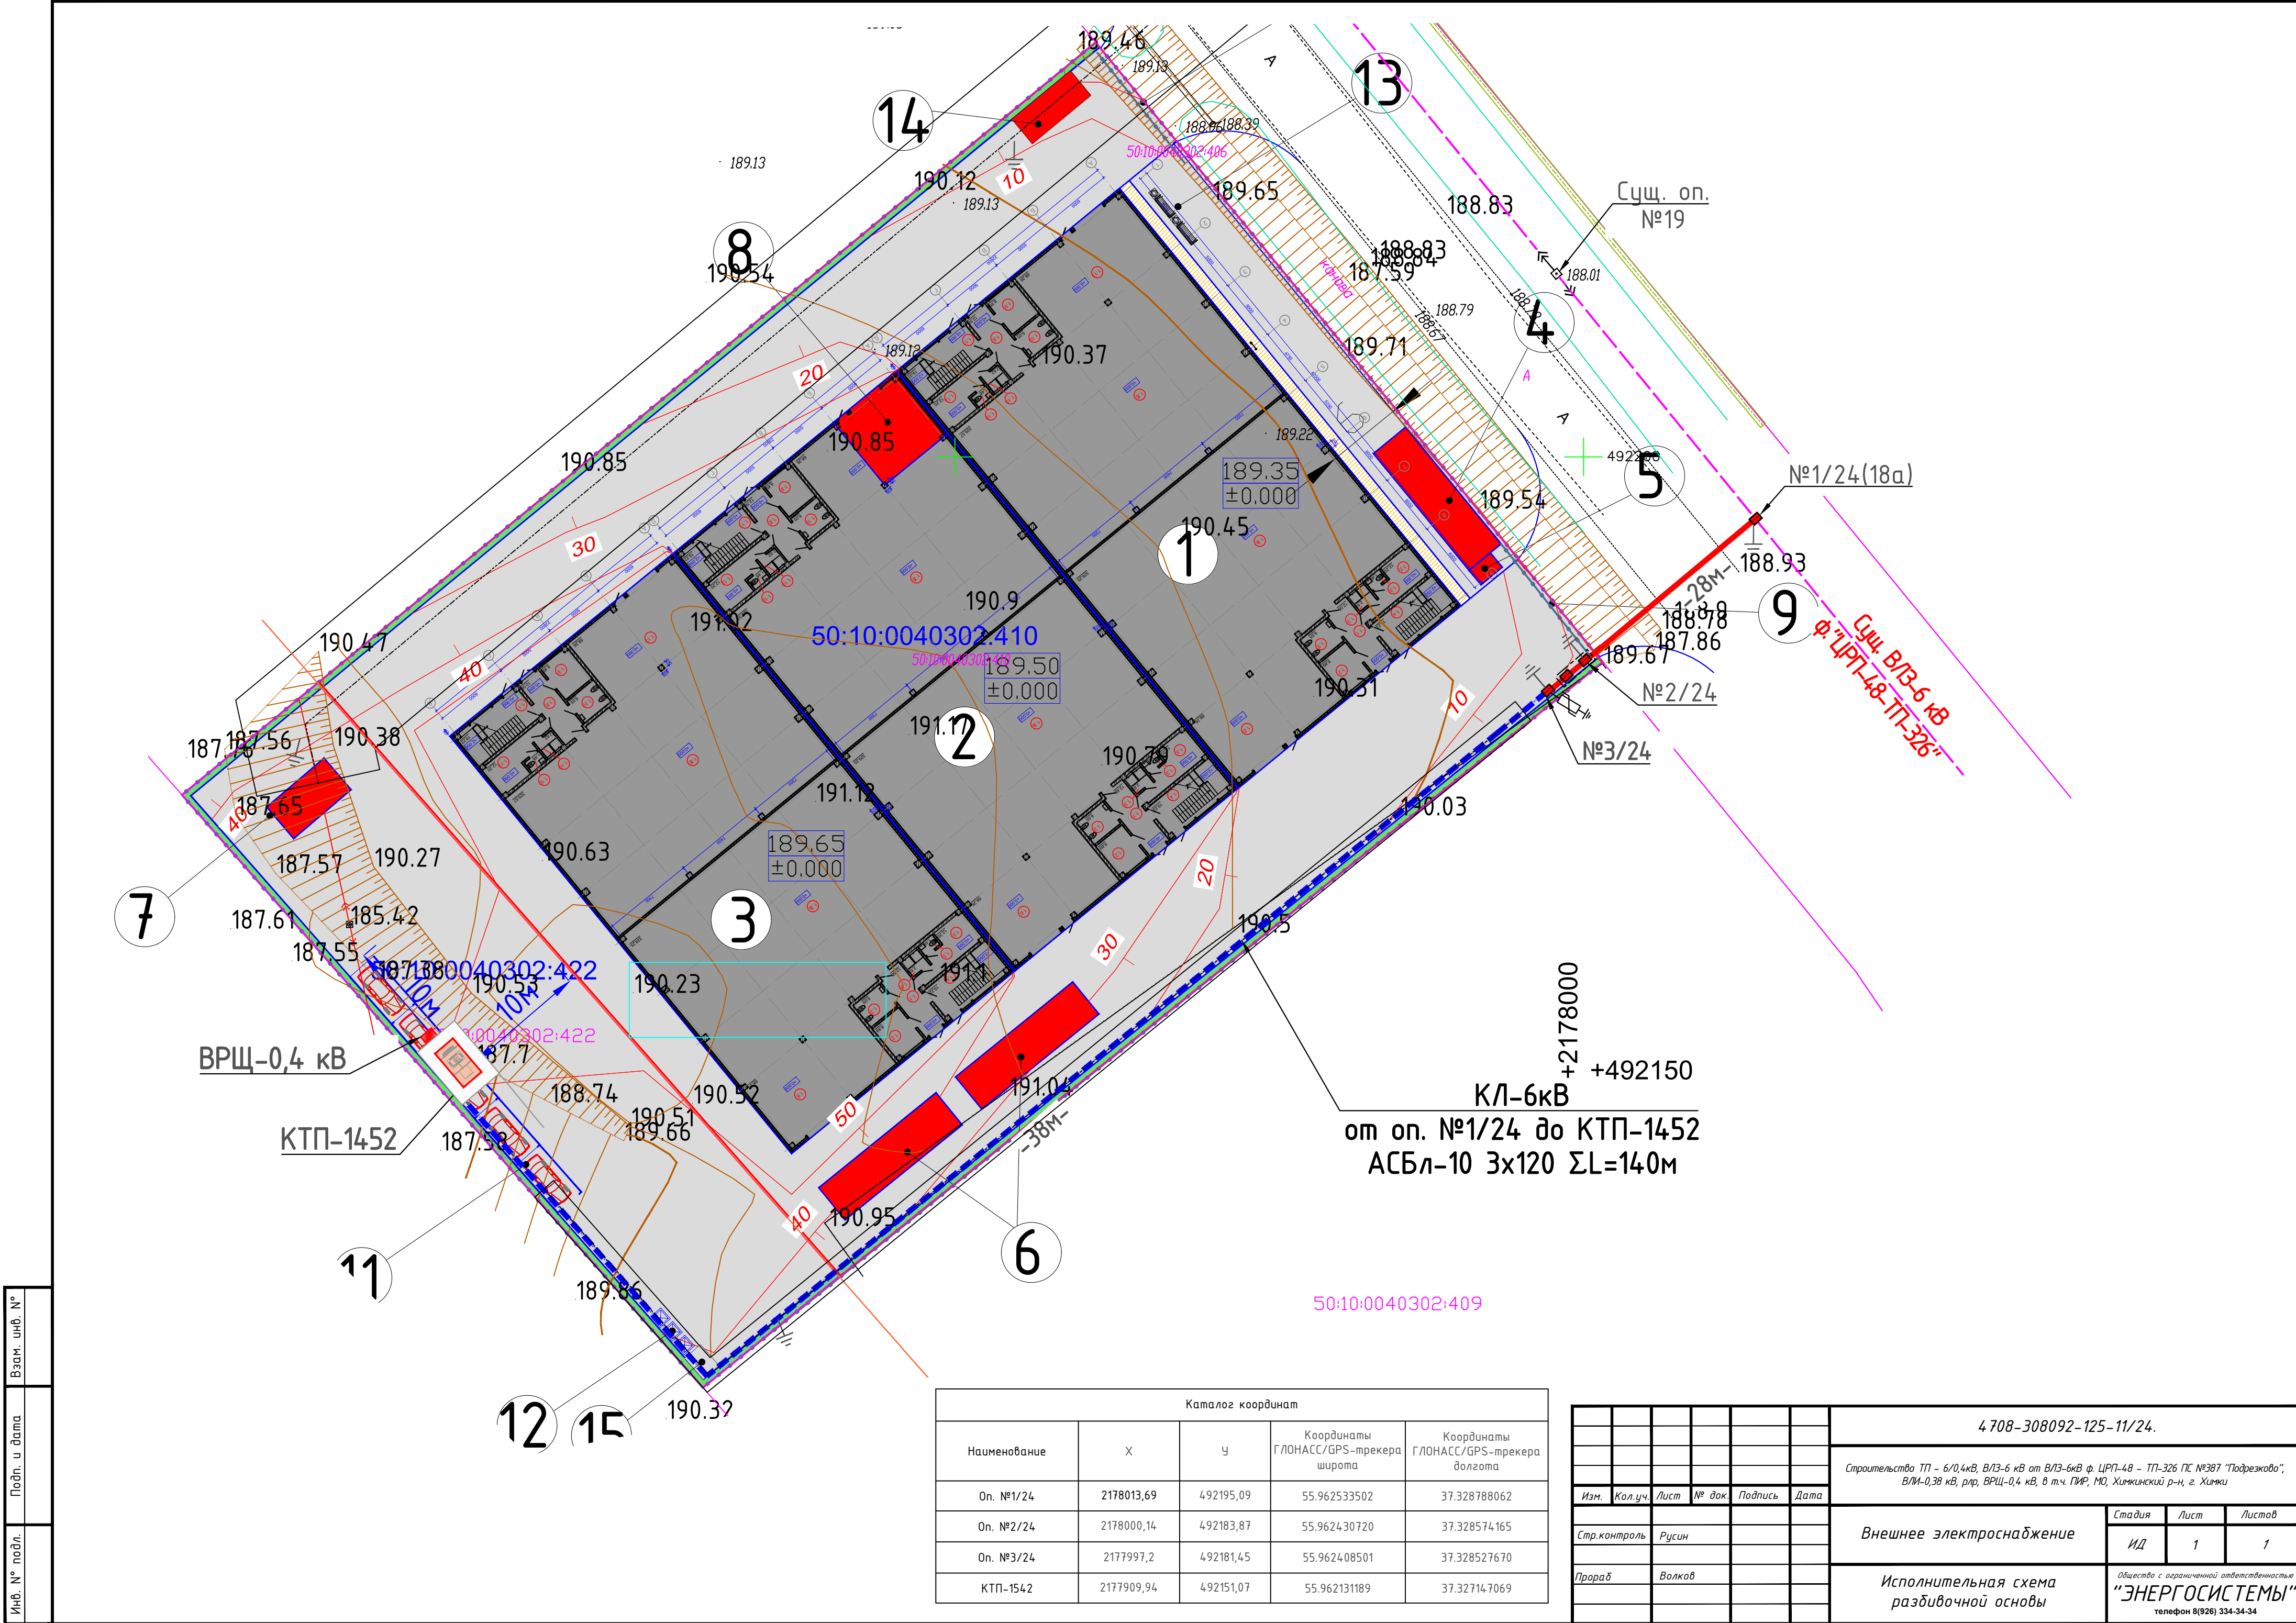

Инф. № подл.	
Подп. и дата	
Взам. инф. №	

Каталог координат				
Наименование	X	Y	Координаты ГЛОНАСС/GPS-трекера широта	Координаты ГЛОНАСС/GPS-трекера долгота
Оп. №1/24	2178013,69	492195,09	55.962533502	37.328788062
Оп. №2/24	2178000,14	492183,87	55.962430720	37.328574165
Оп. №3/24	2177997,2	492181,45	55.962408501	37.328527670
КТП-1542	2177909,94	492151,07	55.962131189	37.327147069

4 708-308092-125-11/24.					
Строительство ТП - 6/0,4кВ, ВЛЗ-6 кВ от ВЛЗ-6кВ ф. ЦРП-4В - ТП-326 ПС №387 "Подрезково", ВЛЗ-0,38 кВ, р/р, ВРЩ-0,4 кВ, в т.ч. ПИР, МО, Химкинский р-н, г. Химки					
Изм.	Кол.уч.	Лист	№ док.	Подпись	Дата
Стр. контроль				Русин	
Прораб				Волков	
Внешнее электроснабжение				ИД	1
Исполнительная схема разбивочной основы				Общество с ограниченной ответственностью "ЭНЕРГОСИСТЕМЫ" телефон 8(926) 334-34-34	